


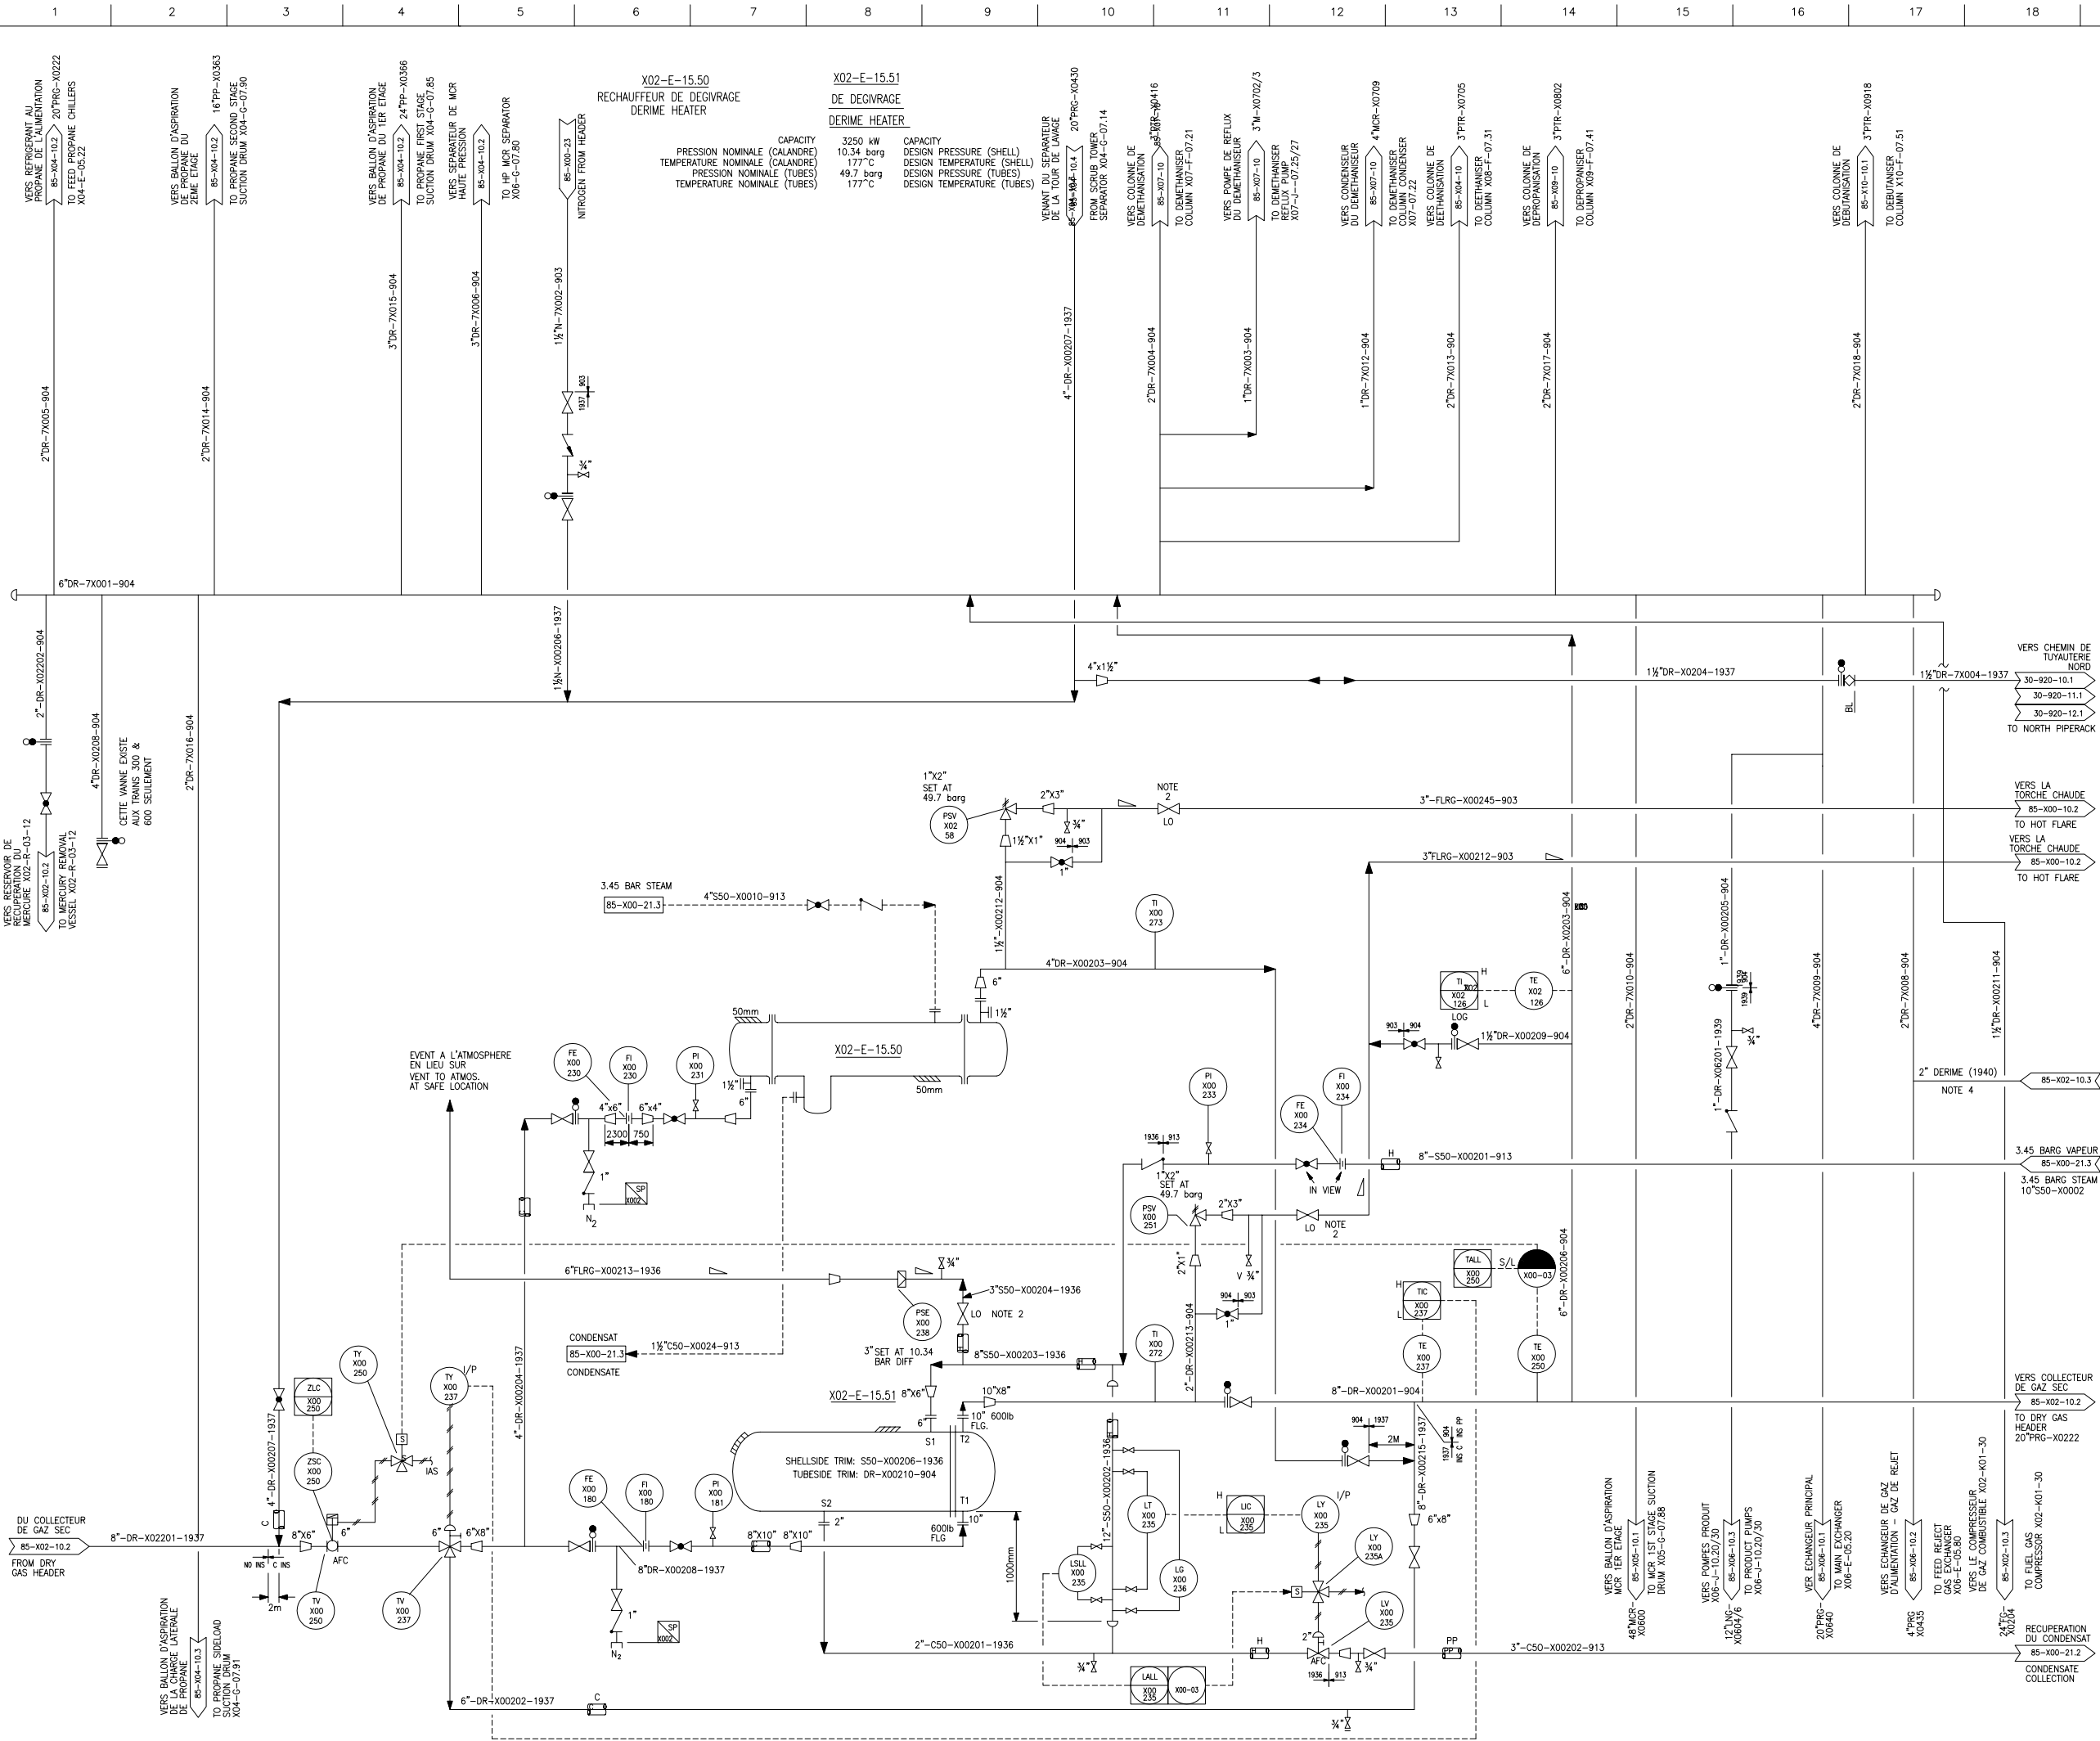

REMARQUES

1. POUR LES SYMBOLES STANDARD DES EQUIPEMENTS, TUYAUTERIES ET INSTRUMENTS, SE REFERER AUX PLANS NO. 00-N-11/12.
2. LES VANNES D'ISOLATION SUR LES CONDUITES DE DECHARGE SERONT OPERATION SERA SOUMISE A UNE PROCEDURE DE CLEF ET . AUTORISATION
3. TOUTS LES CODES DE CLASSIFICATION DE TUYAUTERIE POUR LES NOUVELLES TUYAUTERIE FONT REFERENCE A LA SPECIFICATION 20784-L-001. LE PREFIX "R" EST SOUS-ENTENDU.

NOTES

1. FOR STANDARD SYMBOLS FOR EQUIPMENT, PIPING AND INSTRUMENTS REFER TO DWG's 00-N-11/12.
2. ISOLATING VALVES IN PRESSURE RELIEF LINES SHALL BE KEPT CLOSED OPEN AND SUBJECT TO OPERATION UNDER A KEY AND PERMIT PROCEDURE.
3. ALL PIPING CLASS CODES FOR NEW PIPING REFER TO SPECIFICATION 20784-L-001. THE "R" PREFIX IS IMPLIED.
4. THIS 2" DERIVE LINE IS INSTALLED AT TRAINS 200 AND 600 ONLY. (TEMPORARY INSTALLATION PER JOB NO. S-375).

CE DIAGRAMME REPRESENTA UNE DISPOSITION TYPE DES 6 TRAINS DE
PROCEDE. DES DIFFERENCES MINEURES EXISTANTE SUR CHAQUE TRAIN.

THIS DIAGRAM REPRESENTS A TYPICAL ARRANGEMENT FOR THE 6 PROCESS
TRAINS. MINOR DISSIMILARITIES EXIST ON EACH TRAIN.

CE PLAN EST LA COPIE D'UN DOCUMENT ORIGINAL FOURNI PAR SONATRACH. SON CONTENU TECHNIQUE DEMEURERA LA RESPONSABILITE DE SONATRACH, L'EXCEPTION DES INFORMATIONS COMPLEMENTAIRES ELABOREES PAR BECHTEL POUR LE PROJET DE RENOVATION.

THIS DRAWING IS A COPY OF AN ORIGINAL SONATRACH SUPPLIED DOCUMENT. THE TECHNICAL CONTENT REMAINS THE RESPONSIBILITY OF SONATRACH, EXCEPT TO THE EXTENT THAT THE DRAWING INCORPORATES INFORMATION DEVELOPED BY BECHTEL FOR THE RENOVATION PROJECT.

CE SCHEMA DES TUYAUTERIES ET INSTRUMENTATION EST DERIVE DES PLANS
THIS PIPING AND INSTRUMENTATION DIAGRAM IS DERIVED FROM:
85-X00-25 REV.1

[illegible]

BECHTEL LI
LONDON

SONATRACH UNITE GNL
RENOVATION COMPLEXE GL1.Z
BETHIOUA-ALGERIE

SCHEMA DES TUYAUTERIES ET INSTRUMENTATION :PROCED
UNITE DE LIQUEFACTION DEGIVRAGE
SYSTEME

PROCESS : PIPING & INSTRUMENT DIAGRAM
LIQUEFACTION UNIT DERIVE SYSTEM

	JOB No.	DRAWING No.	REV.
	20784	85-X00-25	5