


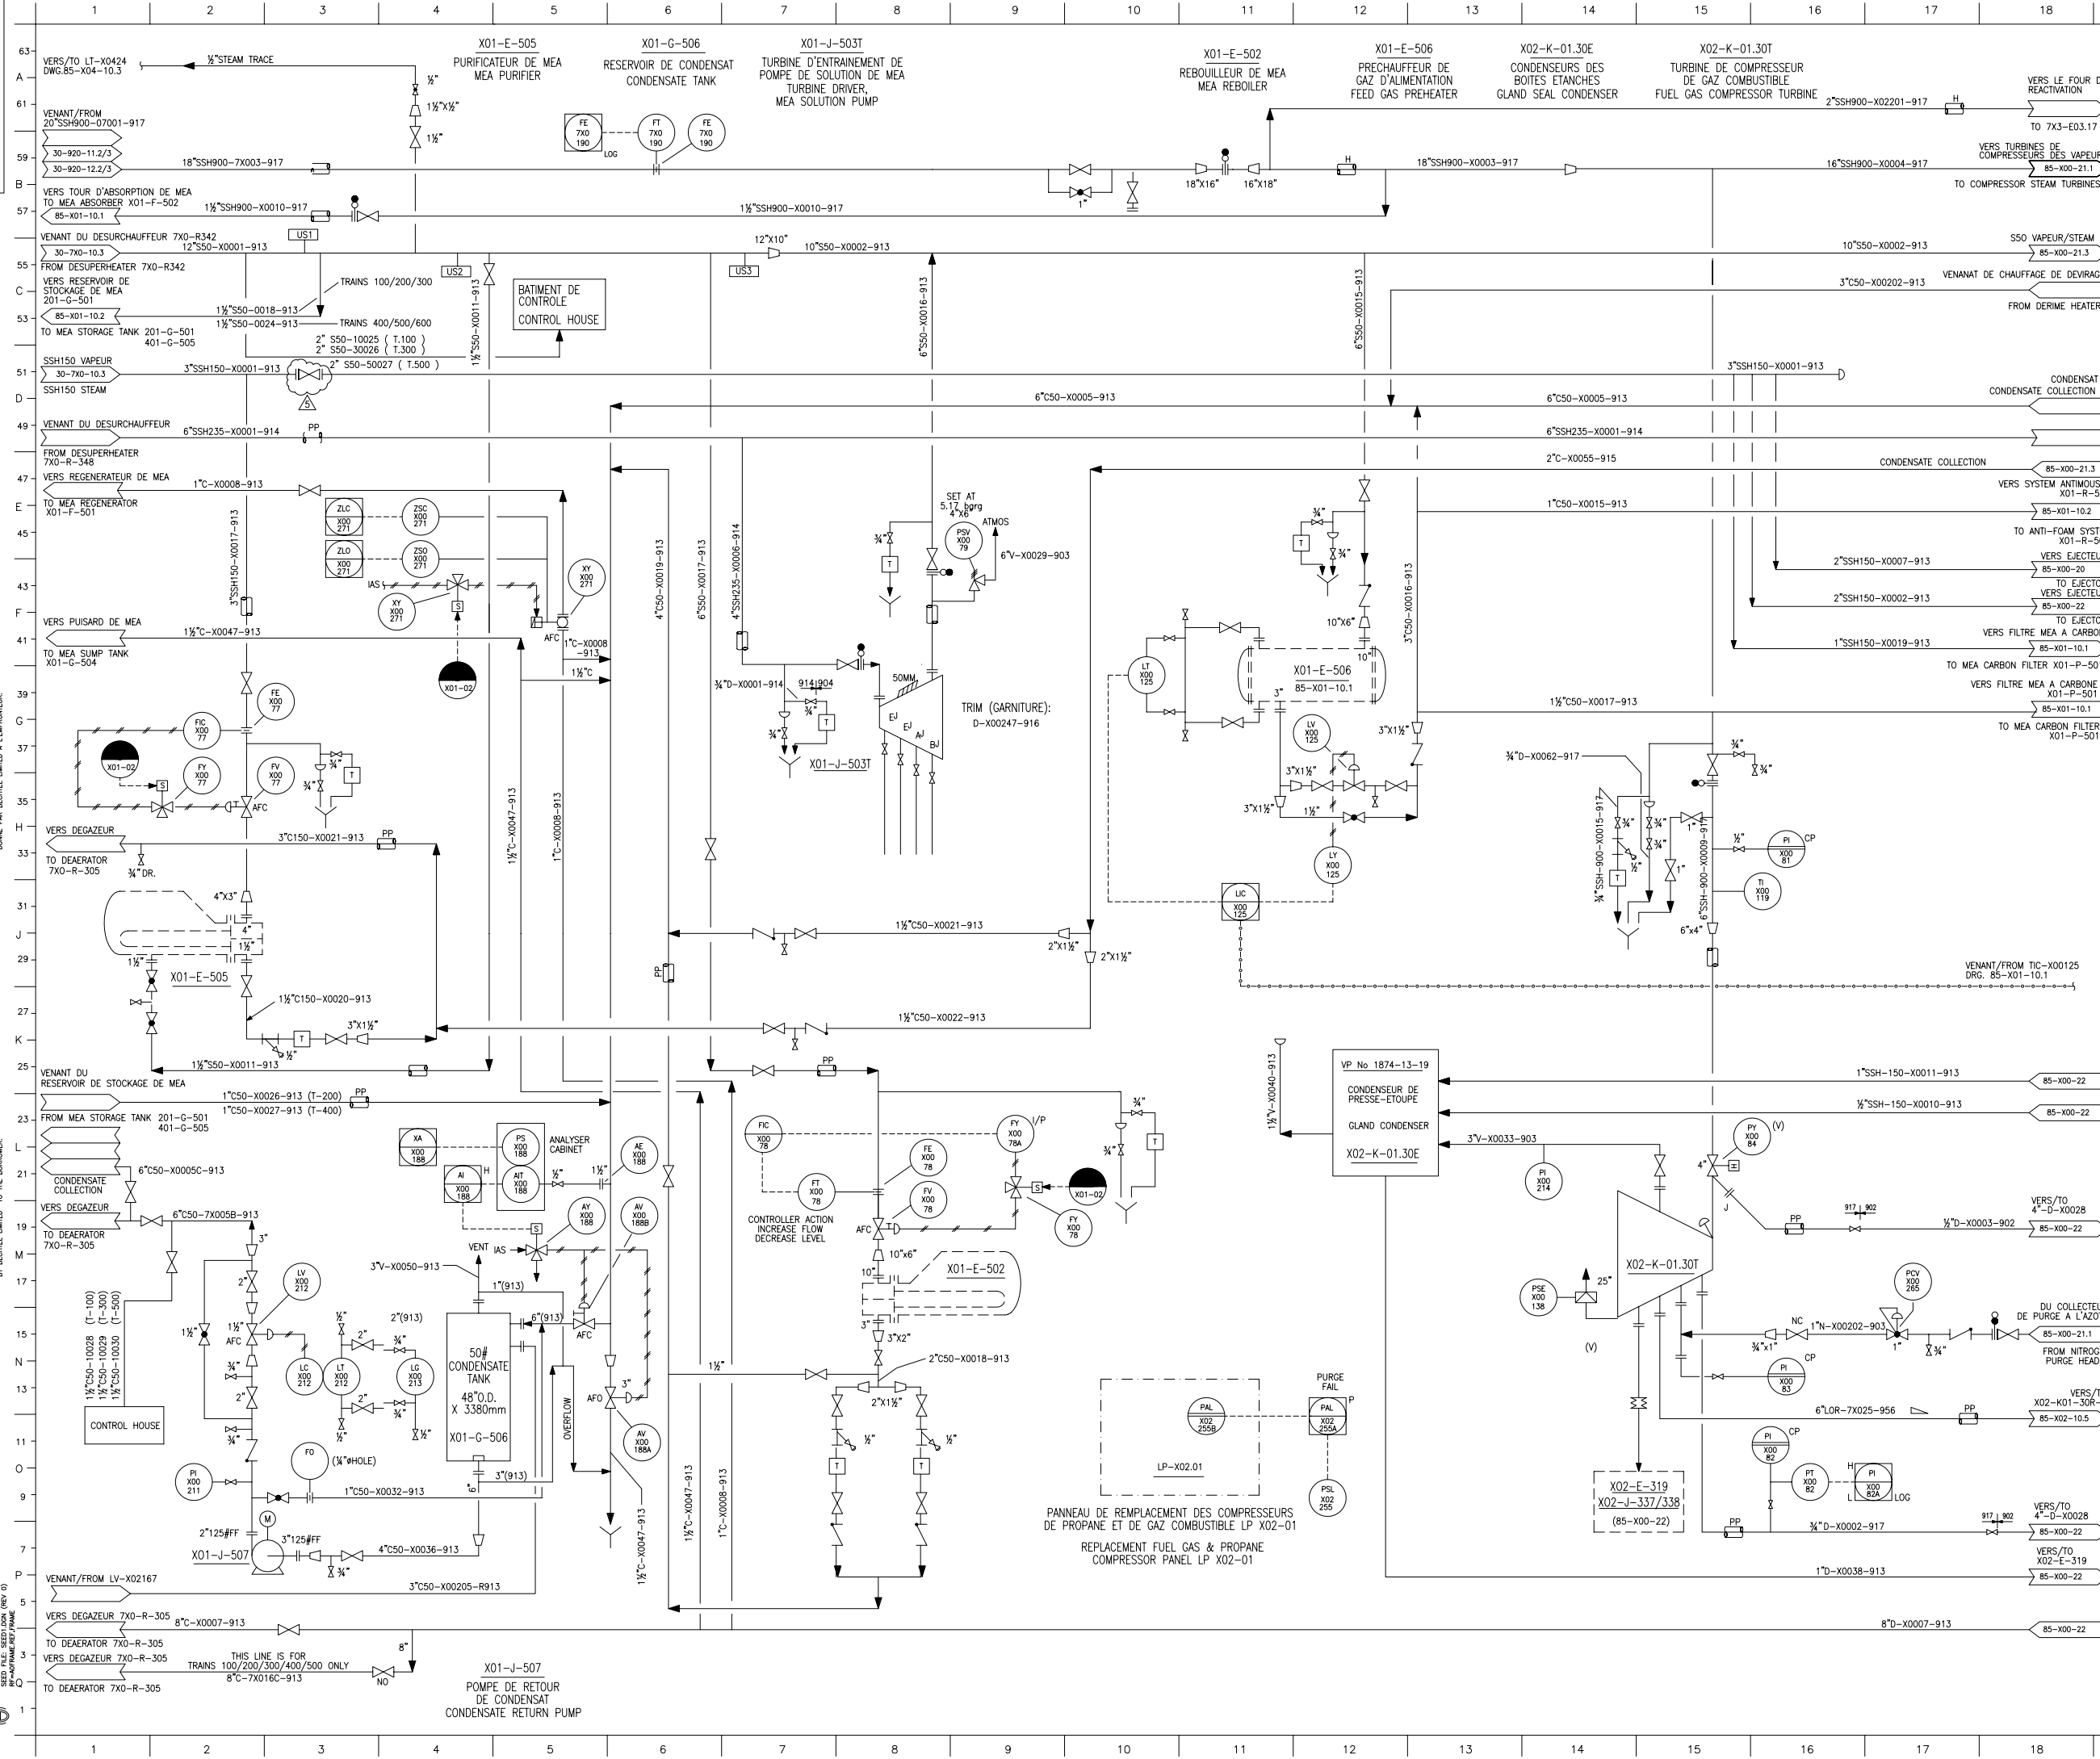

REMARQUES

- POUR LES SYMBOLES STANDARD DES EQUIPEMENTS, TUYAUTERIES ET INSTRUMENTS, SE REFERER AUX PLANS NO. 00-N-11/12
- POUR LES DETAILS DE LA TUYAUTERIE DES TORCHES ET D'ELIMINATION DANS LA SECTION DE LIQUEFACTION VOIR LE P & ID 85-X00-10.3

NOTES

- FOR STANDARD SYMBOLS FOR EQUIPMENT, PIPING AND INSTRUMENTS REFER TO DWG's 00-N-11/12
- FOR DETAILS OF FLARE AND DISPOSAL PIPING IN THE LIQUEFACTION SECTION REFER TO P&ID 85-X00-10.3.

CE DIAGRAMME REPRESENTS UNE DISPOSITION TYPE DES 6 TRAINS DE
PROCEDURE. DES DIFFERENCES MINIEURES EXISTANTE SUR CHAQUE TRAIN.
THIS DIAGRAM REPRESENTS A TYPICAL ARRANGEMENT FOR THE 6 PROCESS.
TRAINS. MINOR DISSIMILARITIES EXIST ON EACH TRAIN.

CE PLAN EST LA COPIE D'UN DOCUMENT ORIGINAL FOURNI PAR SONATRACH.
SON CONTENU TECHNIQUE DEMEURE LA RESPONSABILITE DE SONATRACH.
L'EXCEPTION DES INFORMATIONS COMPLEMENTAIRES ELABOREES PAR BECHTEL
POUR LE PROJET DE RENOVATION.
THIS DRAWING IS A COPY OF AN ORIGINAL SONATRACH SUPPLIED DOCUMENT.
THE TECHNICAL CONTENT REMAINS THE RESPONSIBILITY OF SONATRACH,
EXCEPT TO THE EXTENT THAT THE DRAWING INCORPORATES INFORMATION
DEVELOPED BY BECHTEL FOR THE RENOVATION PROJECT.

CE SCHEMA DES TUYAUTERIES ET INSTRUMENTATION EST TIRE DES PLANS:
85-X00-21

REVIEW APPROVALS									
PIPING	INST	PROCESS	LOGS	START	MECH	M & QS	CH. SYS.	ENG	CLIENT
20-04	20-04	20-04	20-04	20-04	20-04	20-04	20-04	20-04	20-04
20-04	20-04	20-04	20-04	20-04	20-04	20-04	20-04	20-04	20-04
BECHTEL LIMITED
LONDON

SONATRACH UNITE GNL
RENOVATION COMPLEXE GL1.2
BETHIOUA, ALGERIE

SONATRACH LNG PLANT
GL1.2 RENOVATION
BETHIOUA, ALGERIA

SCHEMA DES TUYAUTERIES ET INSTRUMENTATION : PROCEDE
SYSTEME DE VAPEUR ET CONDENSAT

PROCESS : PIPING & INSTRUMENT DIAGRAM
STEAM AND CONDENSATE SYSTEM

JOB No.	DRAWING No.	REV.
20784	85-X00-21.2	5

PLOT TIME: \$\$\$\$\$\$SYTIME\$\$\$\$\$\$